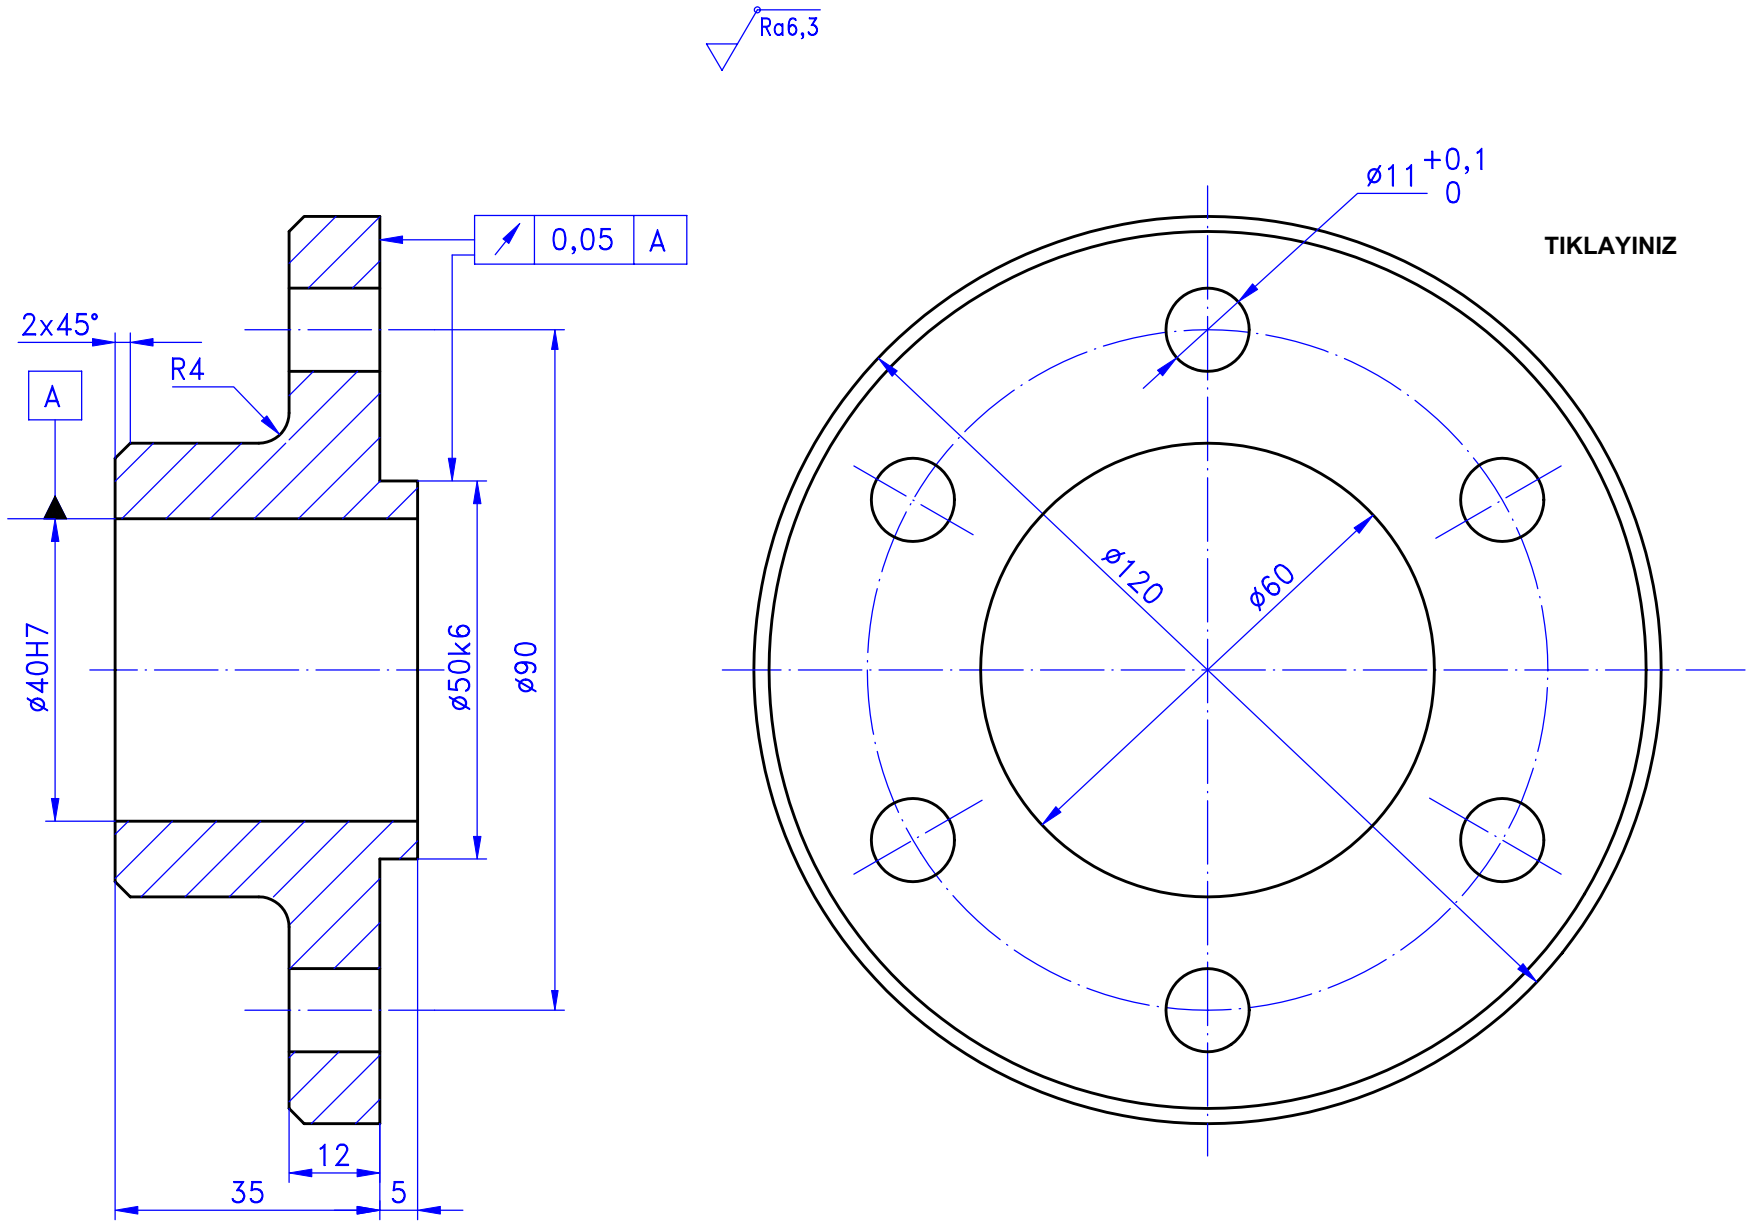


TOL	EBÖ	EKÖ
40H7		
50k6		